

Отчёт сформирован сервисом Контур.Недвижимость согласно записям из ЕГРН,
носит справочный характер и не является официальной выпиской
Отчёт об объекте недвижимости

Сведения о характеристиках объекта недвижимости

Раздел 1 Лист 1

Земельный участок			
вид объекта недвижимости			
Лист № 1 раздела 1	Всего листов раздела 1: 3	Всего разделов: 8	Всего листов отчёта: 16
30.09.2025г. № КУВИ-001/2025-182933097			
Кадастровый номер:	77:09:0005013:9216		
Номер кадастрового квартала:	77:09:0005013		
Дата присвоения кадастрового номера:	14.11.2012		
Ранее присвоенный государственный учетный номер:	данные отсутствуют		
Адрес:	Российская Федерация, город Москва, вн.тер.г. муниципальный округ Хорошевский, шоссе Хорошёвское, земельный участок 32/3		
Площадь:	3020 +/- 19		
Кадастровая стоимость, руб.:	247309883.8		
Кадастровые номера расположенных в пределах земельного участка объектов недвижимости:	77:09:0005009:4999, 77:09:0005013:1106, 77:09:0005013:10637		
Кадастровые номера объектов недвижимости, из которых образован объект недвижимости:	данные отсутствуют		
Кадастровые номера образованных объектов недвижимости:	данные отсутствуют		
Категория земель:	Земли населенных пунктов		
Виды разрешенного использования:	объекты размещения офисных помещений, деловых центров с несколькими функциями (1.2.7)		
Сведения о кадастровом инженере:	Вишнякова Татьяна Александровна, дата завершения кадастровых работ: 26.10.2012		
Сведения о лесах, водных объектах и об иных природных объектах, расположенных в пределах земельного участка:	данные отсутствуют		
Сведения о том, что земельный участок полностью расположен в границах зоны с особыми условиями использования территории, территории объекта культурного наследия, публичного сервитута:	данные отсутствуют		
Сведения о том, что земельный участок расположен в границах особой экономической зоны, территории опережающего развития, зоны территориального развития в Российской Федерации, игровой зоны:	данные отсутствуют		

Земельный участок			
вид объекта недвижимости			
Лист № 2 раздела 1	Всего листов раздела 1: 3	Всего разделов: 8	Всего листов отчёта: 16
30.09.2025г. № КУВИ-001/2025-182933097			
Кадастровый номер:		77:09:0005013:9216	
Сведения о том, что земельный участок расположен в границах особо охраняемой природной территории, Байкальской природной территории и ее экологических зон, лесопарковом зеленом поясе, охотничьего угодья, лесничества:		данные отсутствуют	
Сведения о расположении земельного участка и (или) расположенного на нем объекта недвижимости в границах территории, в отношении которой принято решение о резервировании земель для государственных или муниципальных нужд:		данные отсутствуют	
Сведения о результатах проведения государственного земельного надзора:		данные отсутствуют	
Сведения о расположении земельного участка в границах территории, в отношении которой утвержден проект межевания территории:		данные отсутствуют	
Условный номер земельного участка:		данные отсутствуют	
Сведения о принятии акта и (или) заключении договора, предусматривающих предоставление в соответствии с земельным законодательством исполнительным органом государственным органом власти или органом местного самоуправления, находящегося в государственной или муниципальной собственности земельного участка для строительства наемного дома социального использования или наемного дома коммерческого использования:		данные отсутствуют	
Сведения о том, что земельный участок или земельные участки образованы на основании решения об изъятии земельного участка и (или) расположенного на нем объекта недвижимости для государственных или муниципальных нужд:		данные отсутствуют	
Сведения о том, что земельный участок образован из земель или земельного участка, государственная собственность на которые не разграничена:		данные отсутствуют	
Сведения о наличии земельного спора о местоположении границ земельных участков:		данные отсутствуют	
Статус записи об объекте недвижимости:		Сведения об объекте недвижимости имеют статус "актуальные"	
Особые отметки:		Для данного земельного участка обеспечен доступ посредством земельного участка (земельных участков) с кадастровым номером (кадастровыми номерами): 77:09:0005013:147. Сведения об	

Земельный участок			
вид объекта недвижимости			
Лист № 3 раздела 1	Всего листов раздела 1: 3	Всего разделов: 8	Всего листов отчёта: 16
30.09.2025г. № КУВИ-001/2025-182933097			
Кадастровый номер:		77:09:0005013:9216	
		ограничения права на объект недвижимости, обременениях данного объекта, не зарегистрированных в реестре прав, ограничений прав и обременений недвижимого имущества: вид ограничения (обременения): ограничения прав на земельный участок, предусмотренные статьей 56 Земельного кодекса Российской Федерации; срок действия: с 26.08.2019; реквизиты документа-основания: доверенность от 02.07.2019 № 1946282 выдан: Командир ФКУ "Войсковая часть 28178" Лискин Борис Александрович. вид ограничения (обременения): ограничения прав на земельный участок, предусмотренные статьей 56 Земельного кодекса Российской Федерации; срок действия: с 22.01.2021; реквизиты документа-основания: постановление от 28.12.1999 № 1215 выдан: Правительство Москвы; иКЭС при МКН Протокол секции № 1 "Историко-культурная экспертиза объектов" от 04.12.2008 № 1/31 выдан: Москомнаследие; распоряжение от 18.11.2020 № 791 выдан: Департамент культурного наследия города Москвы.	

Отчёт об объекте недвижимости
Сведения о зарегистрированных правах

Земельный участок			
вид объекта недвижимости			
Лист № 1 раздела 2		Всего листов раздела 2: 3	Всего разделов: 8
Всего листов отчёта: 16			
30.09.2025г. № КУВИ-001/2025-182933097			
Кадастровый номер:		77:09:0005013:9216	
1	Правообладатель (правообладатели):	1.1	Акционерное общество "Ремонтно- эксплуатационное управление", ИНН: 7714783092
	Сведения о возможности предоставления третьим лицам персональных данных физического лица:	1.1.1	данные отсутствуют
2	Вид, номер, дата и время государственной регистрации права:	2.1	Собственность 77:09:0005013:9216-77/051/2022-17 11.08.2022 19:15:46
3	Сведения об осуществлении государственной регистрации сделки, права без необходимого в силу закона согласия третьего лица, органа:	3.1	данные отсутствуют
4	Ограничение прав и обременение объекта недвижимости:		
	4.1 вид:	Запрещение регистрации	
	дата государственной регистрации:	18.09.2025 19:13:02	
	номер государственной регистрации:	77:09:0005013:9216-77/055/2025-27	
	срок, на который установлены ограничение прав и обременение объекта недвижимости:	не установлен	
	лицо, в пользу которого установлены ограничение прав и обременение объекта недвижимости:	не определено	
	сведения о возможности предоставления третьим лицам персональных данных физического лица	данные отсутствуют	
	основание государственной регистрации:	Постановление судебного пристава-исполнителя МОСП по ВАШ № 3, № 1653101083/7747 (491764/25/77047-ИП), выдан 17.07.2025, МОСП по ВАШ № 3	
	сведения об осуществлении государственной регистрации сделки, права, ограничения права без необходимого в силу закона согласия третьего лица, органа:	данные отсутствуют	
	сведения об управляющем залогом и о договоре управления залогом, если такой договор заключен для управления ипотекой:	данные отсутствуют	
	сведения о депозитарии, который осуществляет хранение обездвиженной документарной закладной или электронной закладной:		

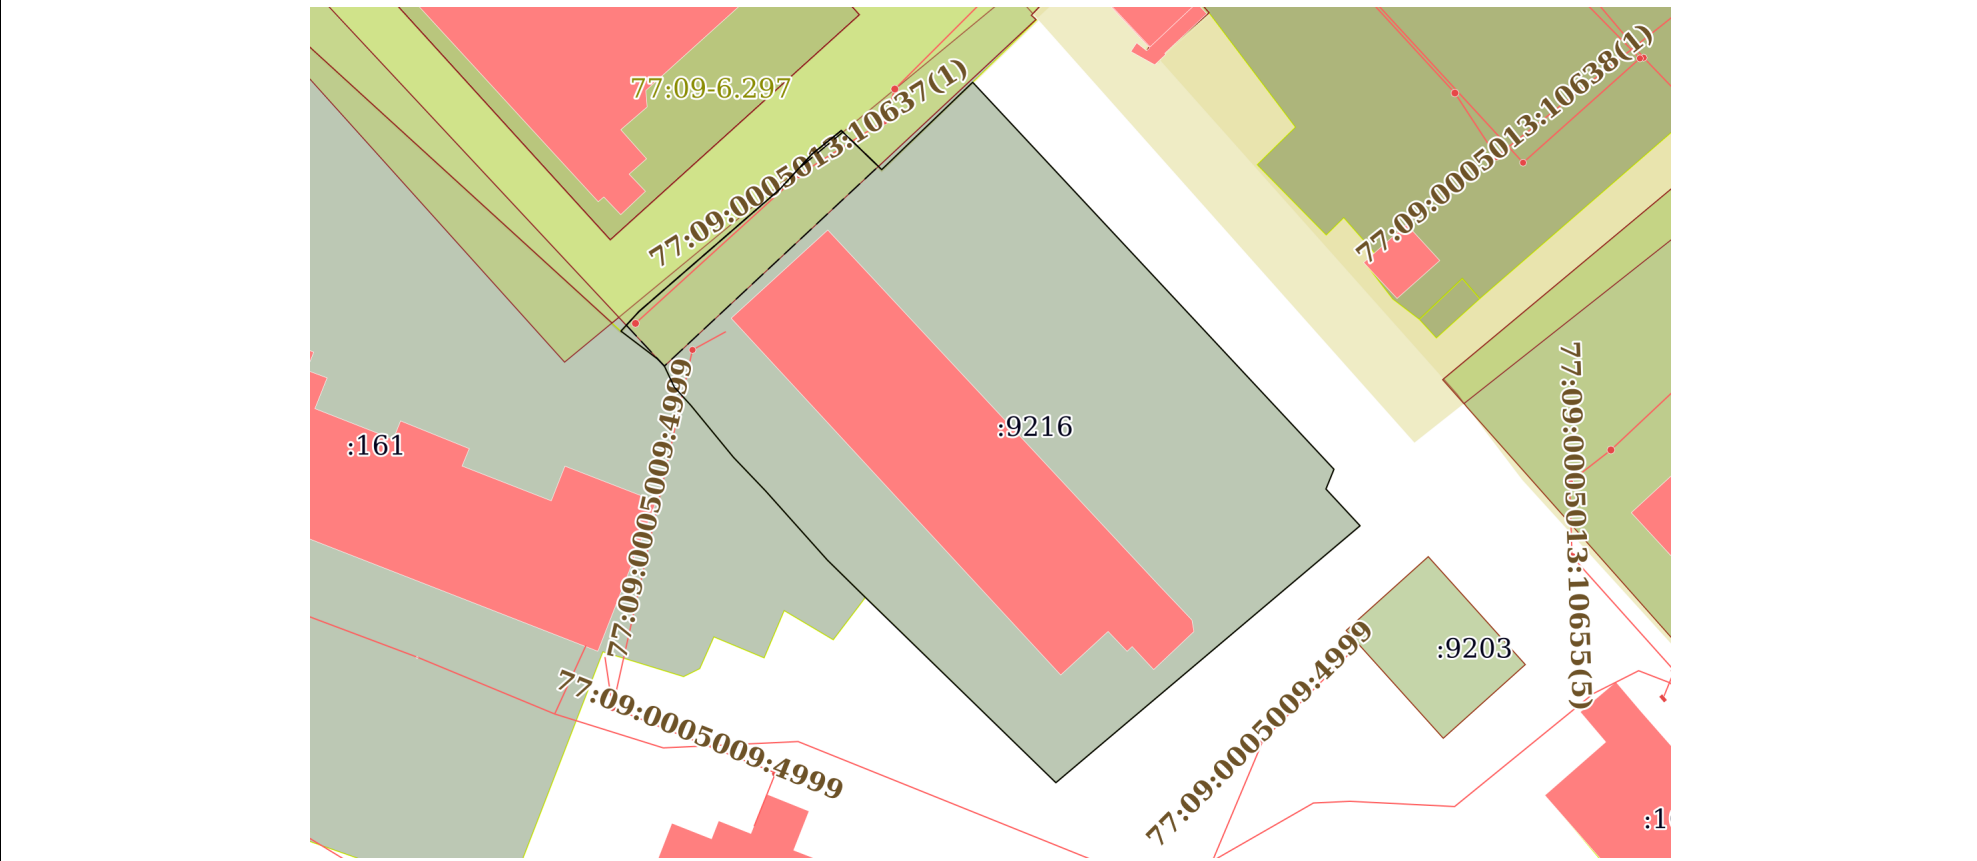
Земельный участок		
вид объекта недвижимости		
Лист № 2 раздела 2	Всего листов раздела 2: 3	Всего разделов: 8
Всего листов отчёта: 16		
30.09.2025г. № КУВИ-001/2025-182933097		
Кадастровый номер:		77:09:0005013:9216
	ведения о внесении изменений или дополнений в регистрационную запись об ипотеке:	
4.2	вид:	Запрещение регистрации
	дата государственной регистрации:	30.06.2025 10:49:43
	номер государственной регистрации:	77:09:0005013:9216-77/055/2025-25
	срок, на который установлены ограничение прав и обременение объекта недвижимости:	не установлен
	лицо, в пользу которого установлены ограничение прав и обременение объекта недвижимости:	не определено
	сведения о возможности предоставления третьим лицам персональных данных физического лица	данные отсутствуют
	основание государственной регистрации:	Постановление судебного пристава-исполнителя СОСП по Ростовской области, № 1931857278/9861 (3836/23/98061-ИП), выдан 25.06.2025, СОСП по Ростовской области
	сведения об осуществлении государственной регистрации сделки, права, ограничения права без необходимого в силу закона согласия третьего лица, органа:	данные отсутствуют
	сведения об управляющем залогом и о договоре управления залогом, если такой договор заключен для управления ипотекой:	данные отсутствуют
	сведения о депозитарии, который осуществляет хранение обездвиженной документарной закладной или электронной закладной:	
	ведения о внесении изменений или дополнений в регистрационную запись об ипотеке:	
5	Договоры участия в долевом строительстве:	не зарегистрировано
6	Заявленные в судебном порядке права требования:	данные отсутствуют
7	Сведения о возможности предоставления третьим лицам персональных данных физического лица	данные отсутствуют
8	Сведения о возражении в отношении зарегистрированного права:	данные отсутствуют
9	Сведения о наличии решения об изъятии объекта недвижимости для государственных и муниципальных нужд:	данные отсутствуют

Земельный участок			
вид объекта недвижимости			
Лист № 3 раздела 2	Всего листов раздела 2: 3	Всего разделов: 8	Всего листов отчёта: 16
30.09.2025г. № КУВИ-001/2025-182933097			
Кадастровый номер:		77:09:0005013:9216	
10	Сведения о невозможности государственной регистрации без личного участия правообладателя или его законного представителя:	данные отсутствуют	
11	Правопритязания и сведения о наличии поступивших, но не рассмотренных заявлений о проведении государственной регистрации права (перехода, прекращения права), ограничения права или обременения объекта недвижимости, сделки в отношении объекта недвижимости:	отсутствуют	
11	Сведения о невозможности государственной регистрации перехода, прекращения, ограничения права на земельный участок из земель сельскохозяйственного назначения:	данные отсутствуют	

Отчёт об объекте недвижимости
Описание местоположения земельного участка

Земельный участок			
вид объекта недвижимости			
Лист № 1 раздела 3	Всего листов раздела 3: 1	Всего разделов: 8	Всего листов отчёта: 16
30.09.2025г. № КУВИ-001/2025-182933097			
Кадастровый номер:		77:09:0005013:9216	

План (чертеж, схема) земельного участка



Масштаб 1:800	Условные обозначения:		
---------------	-----------------------	--	--

Отчёт об объекте недвижимости
Описание местоположения земельного участка

Земельный участок			
вид объекта недвижимости			
Лист № 1 раздела 3.1	Всего листов раздела 3.1: 2	Всего разделов: 8	Всего листов отчёта: 16
30.09.2025г. № КУВИ-001/2025-182933097			
Кадастровый номер:		77:09:0005013:9216	

Описание местоположения границ земельного участка							
№ п/п	Номер точки		Дирекционный угол	Горизонтальное проложение, м	Описание закрепления на местности	Кадастровые номера смежных участков	Сведения об адресах правообладателей смежных земельных участков
	начальная	конечная					
1	2	3	4	5	6	7	8
1	1.1.1	1.1.2	136°58.6`	56.78	данные отсутствуют	данные отсутствуют	данные отсутствуют
2	1.1.2	1.1.3	202°4.8`	2.29	данные отсутствуют	данные отсутствуют	данные отсутствуют
3	1.1.3	1.1.4	137°1.9`	1	данные отсутствуют	данные отсутствуют	данные отсутствуют
4	1.1.4	1.1.5	137°7.7`	4.38	данные отсутствуют	данные отсутствуют	данные отсутствуют
5	1.1.5	1.1.6	229°48.4`	42.7	данные отсутствуют	данные отсутствуют	данные отсутствуют
6	1.1.6	1.1.7	314°13.1`	28.49	данные отсутствуют	данные отсутствуют	данные отсутствуют
7	1.1.7	1.1.8	314°30.3`	5.73	данные отсутствуют	77:09:0005013:161	kiselevns@gmail.com
8	1.1.8	1.1.9	318°13.6`	9.92	данные отсутствуют	77:09:0005013:161	kiselevns@gmail.com
9	1.1.9	1.1.10	316°17.9`	4.99	данные отсутствуют	77:09:0005013:161	kiselevns@gmail.com
10	1.1.10	1.1.11	320°39.2`	7.18	данные отсутствуют	77:09:0005013:161	kiselevns@gmail.com
11	1.1.11	1.1.12	317°52.2`	2.68	данные отсутствуют	77:09:0005013:161	kiselevns@gmail.com
12	1.1.12	1.1.13	334°46.4`	2.49	данные отсутствуют	77:09:0005013:161	kiselevns@gmail.com
13	1.1.13	1.1.14	316°9.2`	1.05	данные отсутствуют	77:09:0005013:161	kiselevns@gmail.com
14	1.1.14	1.1.15	307°15.8`	4.94	данные отсутствуют	77:09:0005013:161	kiselevns@gmail.com
15	1.1.15	1.1.16	42°35.6`	0.84	данные отсутствуют	77:09:0005013:10646, 77:09:0005013:161	адрес отсутствует; kiselevns@gmail.com
16	1.1.16	1.1.17	42°35.8`	2.02	данные отсутствуют	77:09:0005013:10646	адрес отсутствует
17	1.1.17	1.1.18	49°1.7`	20.03	данные отсутствуют	77:09:0005013:10646	адрес отсутствует
18	1.1.18	1.1.19	42°26.5`	5.07	данные отсутствуют	77:09:0005013:10646	адрес отсутствует
19	1.1.19	1.1.20	51°13.7`	4.04	данные отсутствуют	77:09:0005013:10646	адрес отсутствует
20	1.1.20	1.1.21	133°58.4`	5.53	данные отсутствуют	77:09:0005013:10646	адрес отсутствует
21	1.1.21	1.1.22	135°0.0`	0.49	данные отсутствуют	77:09:0005013:10646	адрес отсутствует

Земельный участок							
вид объекта недвижимости							
Лист № 2 раздела 3.1			Всего листов раздела 3.1: 2		Всего разделов: 8		Всего листов отчёта: 16
30.09.2025г. № КУВИ-001/2025-182933097							
Кадастровый номер:				77:09:0005013:9216			
1	2	3	4	5	6	7	8
22	1.1.22	1.1.1	46°10.1`	13.53	данные отсутствуют	77:09:0005013:10646	адрес отсутствует

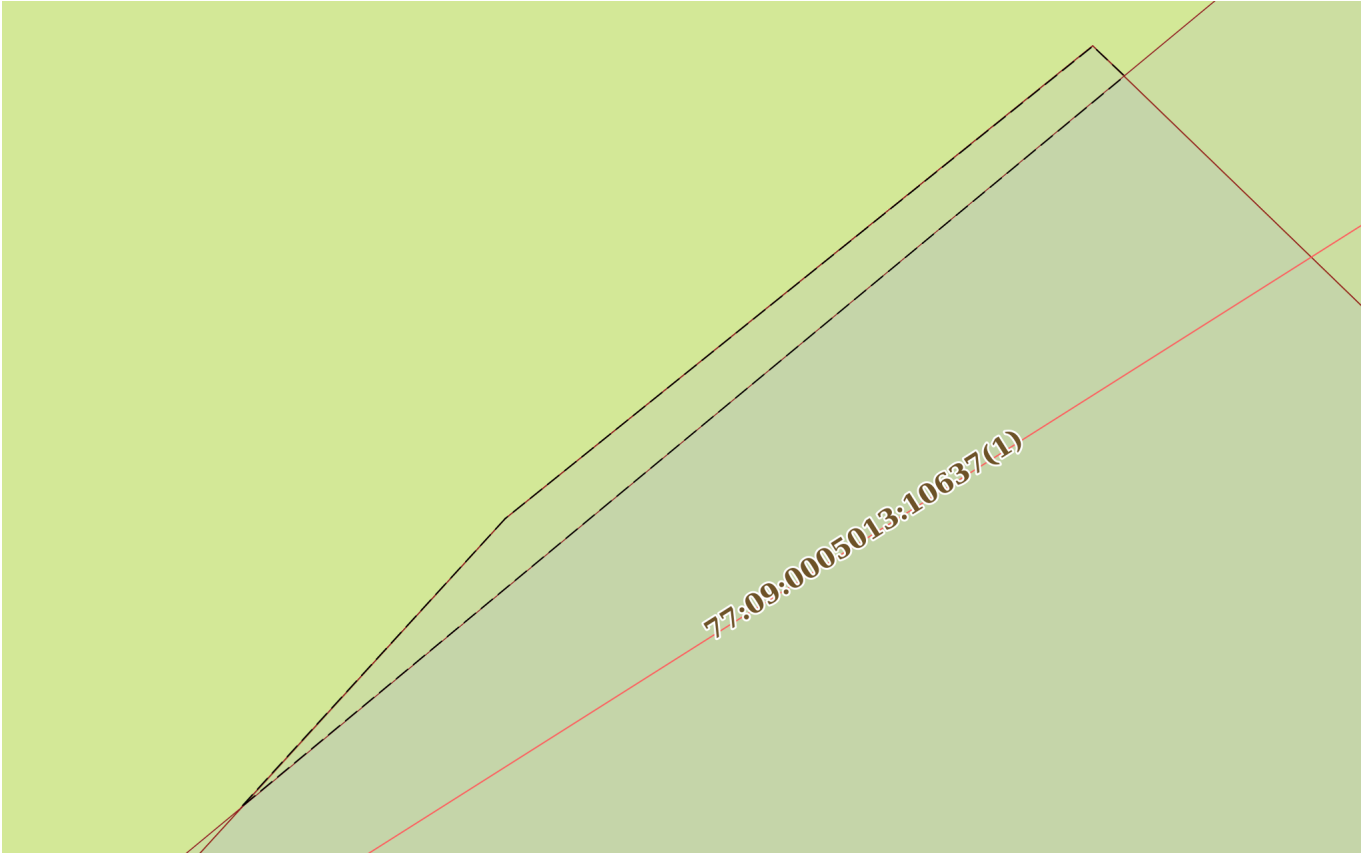
Отчёт об объекте недвижимости
Описание местоположения земельного участка

Земельный участок			
вид объекта недвижимости			
Лист № 1 раздела 3.2	Всего листов раздела 3.2: 2	Всего разделов: 8	Всего листов отчёта: 16
30.09.2025г. № КУВИ-001/2025-182933097			
Кадастровый номер:		77:09:0005013:9216	

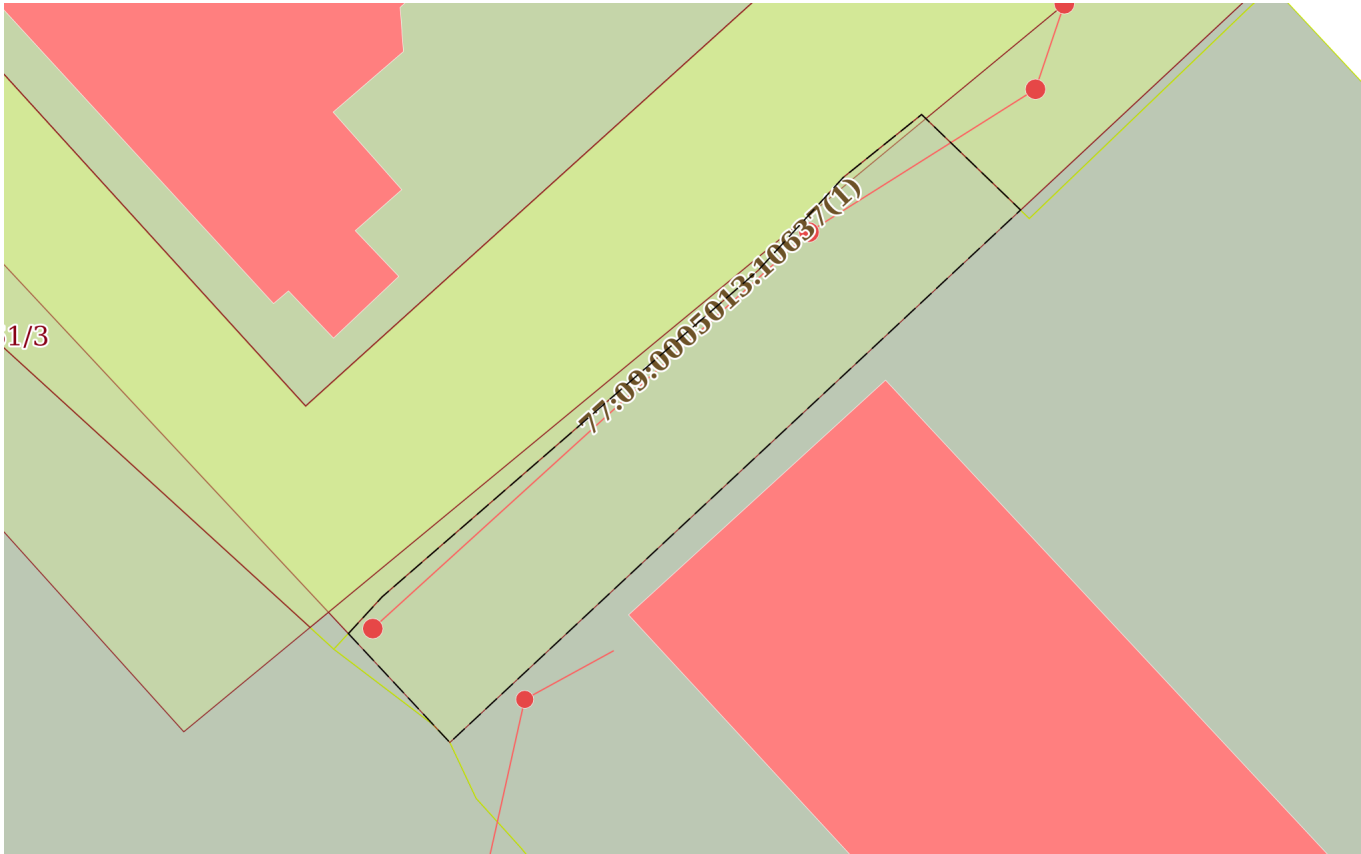
Сведения о характерных точках границы земельного участка				
Система координат ПМСК Москвы				
Номер точки	Координаты, м		Описание закрепления на местности	Средняя квадратичная погрешность определения координат характерных точек границ земельного участка, м
	X	Y		
1	2	3	4	5
1	12089.44	2761.06	Закрепление отсутствует	0.1
2	12047.93	2799.8	Закрепление отсутствует	0.1
3	12045.81	2798.94	Закрепление отсутствует	0.1
4	12045.08	2799.62	Закрепление отсутствует	0.1
5	12041.87	2802.6	Закрепление отсутствует	0.1
6	12014.31	2769.98	Закрепление отсутствует	0.1
7	12034.18	2749.56	Закрепление отсутствует	0.1
8	12038.2	2745.47	Закрепление отсутствует	0.1
9	12045.6	2738.86	Закрепление отсутствует	0.1
10	12049.21	2735.41	Закрепление отсутствует	0.1
11	12054.76	2730.86	Закрепление отсутствует	0.1
12	12056.75	2729.06	Закрепление отсутствует	0.1
13	12059	2728	Закрепление отсутствует	0.1
14	12059.76	2727.27	Закрепление отсутствует	0.1
15	12062.75	2723.34	Закрепление отсутствует	0.1
16	12063.37	2723.91	Закрепление отсутствует	0.1
17	12064.86	2725.28	Закрепление отсутствует	0.1
18	12077.99	2740.4	Закрепление отсутствует	0.1
19	12081.73	2743.82	Закрепление отсутствует	0.1
20	12084.26	2746.97	Закрепление отсутствует	0.1
21	12080.42	2750.95	Закрепление отсутствует	0.1
22	12080.07	2751.3	Закрепление отсутствует	0.1

Земельный участок					
вид объекта недвижимости					
Лист № 2 раздела 3.2		Всего листов раздела 3.2: 2		Всего разделов: 8	Всего листов отчёта: 16
30.09.2025г. № КУВИ-001/2025-182933097					
Кадастровый номер:			77:09:0005013:9216		
1	2	3	4	5	
1	12089.44	2761.06	Закрепление отсутствует	0.1	

Отчёт об объекте недвижимости
Сведения о частях земельного участка

Земельный участок			
вид объекта недвижимости			
Лист № 1 раздела 4	Всего листов раздела 4: 2	Всего разделов: 8	Всего листов отчёта: 16
30.09.2025г. № КУВИ-001/2025-182933097			
Кадастровый номер:		77:09:0005013:9216	
План (чертеж, схема) части земельного участка		Учетный номер части: 77:09:0005013:9216/1	
			
Масштаб 1:40	Условные обозначения:		

Земельный участок			
вид объекта недвижимости			
Лист № 2 раздела 4	Всего листов раздела 4: 2	Всего разделов: 8	Всего листов отчёта: 16
30.09.2025г. № КУВИ-001/2025-182933097			
Кадастровый номер:		77:09:0005013:9216	

План (чертеж, схема) части земельного участка		Учетный номер части: 77:09:0005013:9216/2	
			
Масштаб 1:300	Условные обозначения:		

Отчёт об объекте недвижимости
Сведения о частях земельного участка

Земельный участок			
вид объекта недвижимости			
Лист № 1 раздела 4.1	Всего листов раздела 4.1: 1	Всего разделов: 8	Всего листов отчёта: 16
30.09.2025г. № КУВИ-001/2025-182933097			
Кадастровый номер:		77:09:0005013:9216	
Учетный номер части	Площадь, м2	Содержание ограничения в использовании или ограничения права на объект недвижимости или обременения объекта недвижимости	
1	2	3	
77:09:0005013:9216/1	1	вид ограничения (обременения): ограничения прав на земельный участок, предусмотренные статьей 56 Земельного кодекса Российской Федерации; Срок действия: не установлен; реквизиты документа-основания: доверенность от 02.07.2019 № 1946282 выдан: Командир ФКУ "Войсковая часть 28178" Лискин Борис Александрович; Содержание ограничения (обременения): При строительстве и реконструкции объектов (зданий, сооружений), выделении земельных участков, проведении ландшафтных, рекреационных и иных работ в пределах специальной зоны запрашивать письменное согласование с федеральным казенным учреждением "Войсковая часть 28178". Указанное согласование осуществляется через Правительство Московской области (Постановление Губернатора Московской области от 29.12.2007г. № 179 ПГС, Постановление Правительства Российской Федерации от 05.05.2014г. № 405). Срок действия ограничения: бессрочно.; Реестровый номер границы: 77.09.2.68	
77:09:0005013:9216/2	180	вид ограничения (обременения): ограничения прав на земельный участок, предусмотренные статьей 56 Земельного кодекса Российской Федерации; Срок действия: не установлен; реквизиты документа-основания: постановление от 28.12.1999 № 1215 выдан: Правительство Москвы; иКЭС при МКН Протокол секции № 1 "Историко-культурная экспертиза объектов" от 04.12.2008 № 1/31 выдан: Москомнаследие; распоряжение от 18.11.2020 № 791 выдан: Департамент культурного наследия города Москвы; Содержание ограничения (обременения): Режим использования земель установлен в соответствии с: Постановлением Правительства Москвы № 1215 от 28.12.1999; ИКЭС при МКН Протокол секции № 1 "Историко-культурная экспертиза объектов" № 1/31 от 04.12.2008, Федеральным законом от 25.06.2002 № 73-ФЗ "Об объектах культурного наследия (памятниках истории и культуры) народов Российской Федерации"; Реестровый номер границы: 77:09-6.257; Вид объекта реестра границ: Зона с особыми условиями использования территории; Вид зоны по документу: Зона регулирования застройки № 11; Тип зоны: Зона охраны объекта культурного наследия	

Отчёт об объекте недвижимости
Сведения о частях земельного участка

Земельный участок				
вид объекта недвижимости				
Лист № 1 раздела 4.2		Всего листов раздела 4.2: 2		Всего разделов: 8
Всего листов отчёта: 16				
30.09.2025г. № КУВИ-001/2025-182933097				
Кадастровый номер:			77:09:0005013:9216	
Сведения о характерных точках границы части (частей) земельного участка				
Учетный номер части: 77:09:0005013:9216/1				
Система координат ПМСК Москвы				
Номер точки	Координаты, м		Описание закрепления на местности	Средняя квадратичная погрешность определения координат характерных точек границ земельного участка, м
	X	Y		
1	2	3	4	5
1	12081.73	2743.82	Закрепление отсутствует	0.1
2	12080.18	2742.4	-	-
3	12084.1	2747.14	-	-
4	12084.26	2746.97	Закрепление отсутствует	0.1
1	12081.73	2743.82	Закрепление отсутствует	0.1

Земельный участок				
вид объекта недвижимости				
Лист № 2 раздела 4.2		Всего листов раздела 4.2: 2		Всего разделов: 8
Всего листов отчёта: 16				
30.09.2025г. № КУВИ-001/2025-182933097				
Кадастровый номер:		77:09:0005013:9216		
Сведения о характерных точках границы части (частей) земельного участка				
Учетный номер части: 77:09:0005013:9216/2				
Система координат				
Номер точки	Координаты, м		Описание закрепления на местности	Средняя квадратичная погрешность определения координат характерных точек границ земельного участка, м
	X	Y		
1	2	3	4	5
1	12063.38	2723.92	-	-
2	12064.86	2725.28	-	-
3	12077.99	2740.4	-	-
4	12081.73	2743.82	-	-
5	12084.26	2746.97	-	-
6	12080.42	2750.95	-	-
7	12059	2728	-	-
1	12063.38	2723.92	-	-