

Государственное унитарное предприятие Моск
"Московское областное бюро технической ине
(ГУП МО "МОБТИ")

ГОЛИЦЫНСКИЙ ФИЛИАЛ

Инв. № 179:055-8606

Том 1 прошит



000010233001

ТЕХНИЧЕСКИЙ ПАСПОРТ

на жилой дом
(тип объекта учета)

объект индивидуального жилищного строительства
(наименование объекта)

Адрес (местоположение) объекта

Субъект Российской Федерации Московская обл.

Административный район (округ) Одинцовский р-н

Сельский округ _____

Город (др. поселение) дер. Семенково

Район города _____

Улица (пер.) _____

Дом № / строение (корпус) 17а

Штамп органа государственного технического учета о внесении сведений в Единый государственный реестр объектов капитального строительства

Наименование учетного органа	ГУП МО "МОБТИ"
Инвентарный номер	179:055-8606
Кадастровый номер	
Дата внесения сведений в реестр	

Паспорт составлен по состоянию на 16 апреля 2009 г.

ДИРЕКТОР

М.П.

(подпись)

Кочоян А.С.

ЗОТОВА Т.Г.

(Фамилия И. О.)



5811427

СОДЕРЖАНИЕ:

№ п/п	Наименование раздела, прилагаемых документов:	№ стр.
1	Общие сведения	
2	Состав объекта	
3	Сведения о правообладателях объекта	
4	Ситуационный план	
5	Благоустройство объекта	
6	Позтажный план	
7	Экспликация к поэтажному плану	
8	Отметки об обследованиях	

1. Общие сведения

1	Назначение	<i>жилое</i>
2	Фактическое использование	<i>не по назначению</i>

	Год постройки	Общая площадь жилых помещений, кв. м	Жилая площадь, кв. м	Число этажей надземной части	Число этажей подземной части
	3	4	5	6	7
лит. А жилой дом		1043,2	170,2		
лит. А2 мансарда		491,7			
лит. А1 подвал		473,6			
лит. Б дом-сторожка		225,4	36,8		
ИТОГО		2233,9	207,0		

8	Примечание	<i>Официально присвоенный (почтовый) адрес объекта отсутствует, адрес земельного участка в соответствии со свидетельством о государственной регистрации №50-01/20-30/2004-82 от 07.04.2004г. Сведения о местоположении объекта представлены заявителем. В эксплуатацию не сдано.</i> <i>Разрешение на строительство: Постановление № 427 от 19.04.2004г.; Разрешительное письмо №996/253 от 04.08.2005г.</i>

1.1. Ранее присвоенные (справочно):

Адрес	
Инвентарный номер	
Кадастровый номер	
Литера	


2. Состав объекта

№ на плане (литера)	Наименование зданий, сооружений	Год ввода в эксплуатацию/начала строительства	Материал стен	Параметр			Площадь, застройки кв.м	Высота, м	Объем, куб.м	Инвентаризационная стоимость в ценах на дату составления паспорта, руб.
				наименование параметра	единица измерения	всего				
1	2	3	4	5	6	7	8	9	10	11
A	жилой дом		кирпичные	общая площадь жилых помещений	кв.м	1 043,2	743,6	7,74	5 710	3894852,00
A2	мансарда		деревянные, кирпичные	общая площадь жилых помещений	кв.м	491,7		2,80	2 032	984262,50
A1	подвал		кирпичные	общая площадь жилых помещений	кв.м	473,6		2,10	1 338	1959691,50
a	терраса		металлические	-	-	-	331,1			225985,50
a1	балкон		металлические	-	-	-				6532,50
B	дом-сторожка		кирпичные	общая площадь жилых помещений	кв.м	225,4	171,2	5,92	1 013	847431,00
.	камин			-	-	-				10666,50
..	АОГВ		Водяное отопление	-	-	-				17121,00
									Итого	7946542,50
	служебные строения:									
Г	флигель		кирпичные	-	-	-	132,7	5,41	718	375082,50
									Итого	375082,50
	сооружения:									
Г1	скважина		Артезианский глубиной 116 м, с электронасосом	-	-	-				42393,00
Г2	септик			-	-	-			10	13650,00
№1	забор		деревянные	-	-	-				491439,00
№2	забор		деревянные	-	-	-	120,0			28314,00
									Итого	575796,00
									Всего	8897421,00

3. Сведения о правообладателях объекта

№ п/п	Дата записи	Субъект права: для граждан - фамилия, имя, отчество; паспортные данные; для юридических лиц - наименование в соответствии с уставом	Вид права, правоустанавливающие, правоудостоверяющие документы	Доля (часть, литера)	ФИО лица внесшего запись	Подпись лица внесшего запись
1	2	3	4	5	6	7
1						

СИТУАЦИОННЫЙ ПЛАН
земельного участка
Расположенного в дер. Семенково, дом 17 а

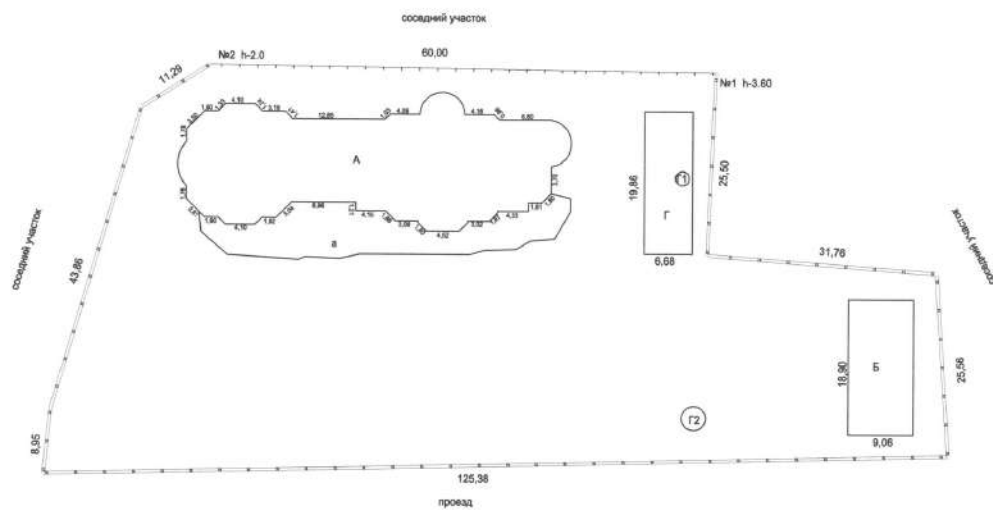

1:500

план составил
16 апреля 2009 г.
Исполнитель Гриндуль В.М.
Проверил Пузанкова О.В.

[Signature]

5. Благоустройство объекта индивидуального жилищного строительства

7

лит. А жилой дом


лит. Б дом-сторожка

Вид благоустройства	Площадь, кв.м
отоп. от АГВ	2233,7
электричество	2233,7

ПОЭТАЖНЫЙ ПЛАН


строения лит. А, в
Находящегося в дер. Семеново, д. 17а

1 Этаж

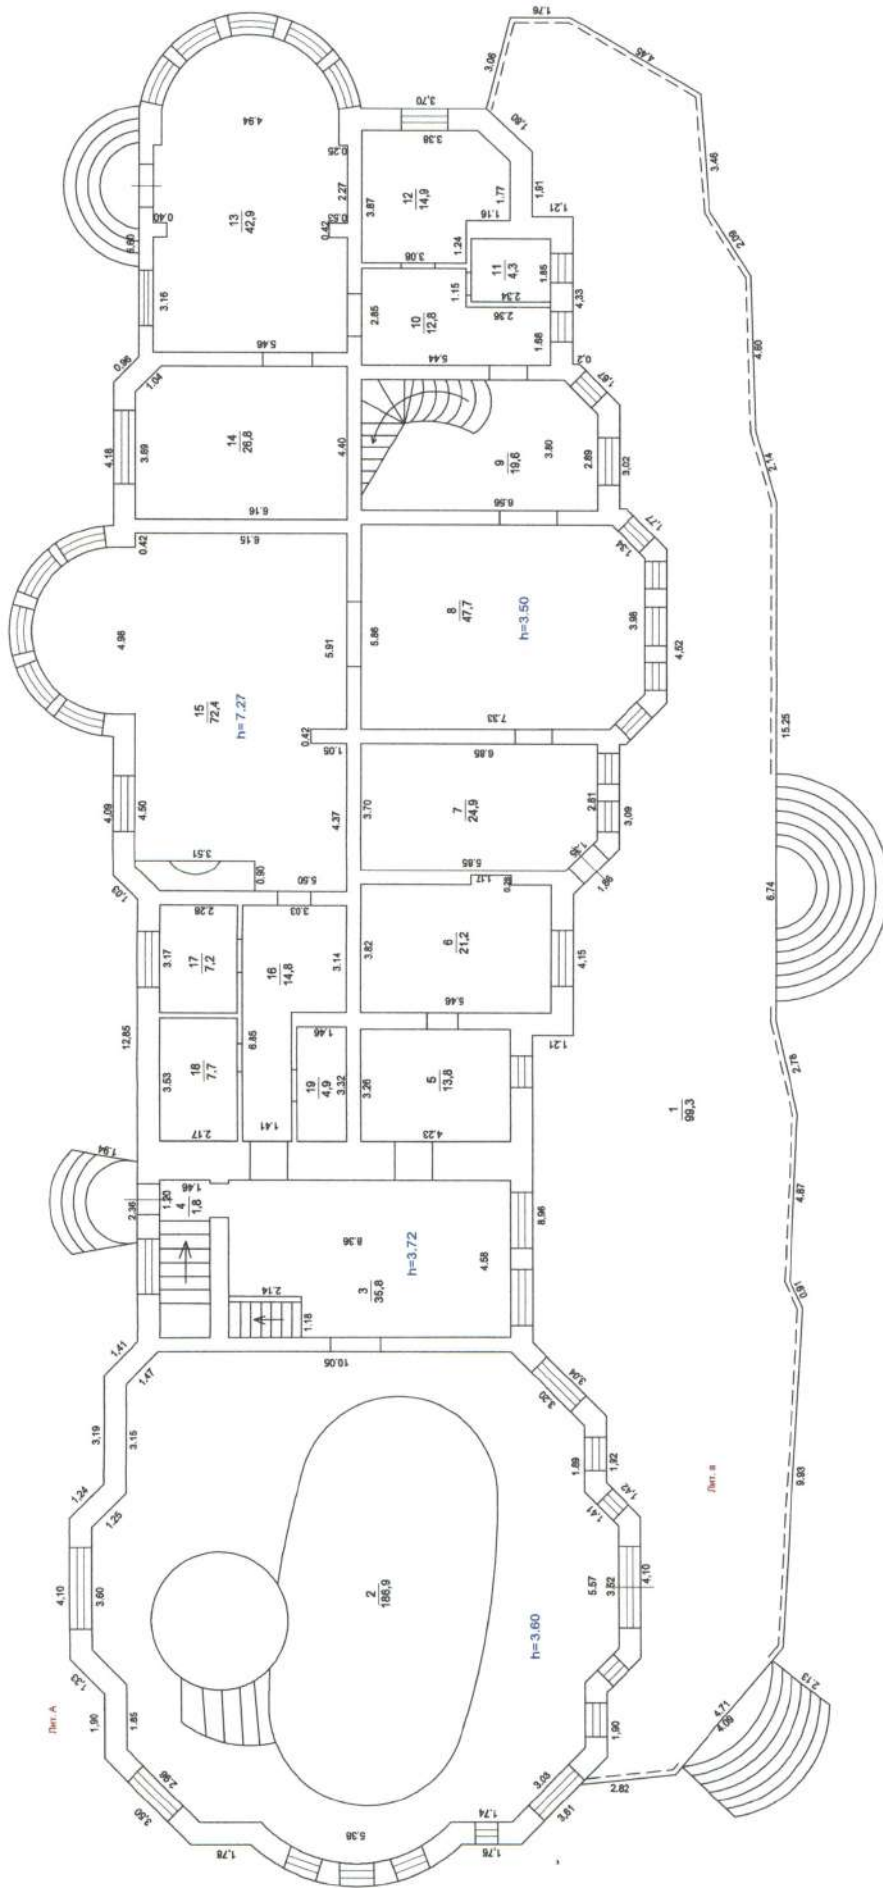

ПЛАН СОСТАВИЛ
" 16 " 04 2009 г.
Исполнил: Гринько В.М.
Проверил: Пузырева О.В.

масштаб 1:150

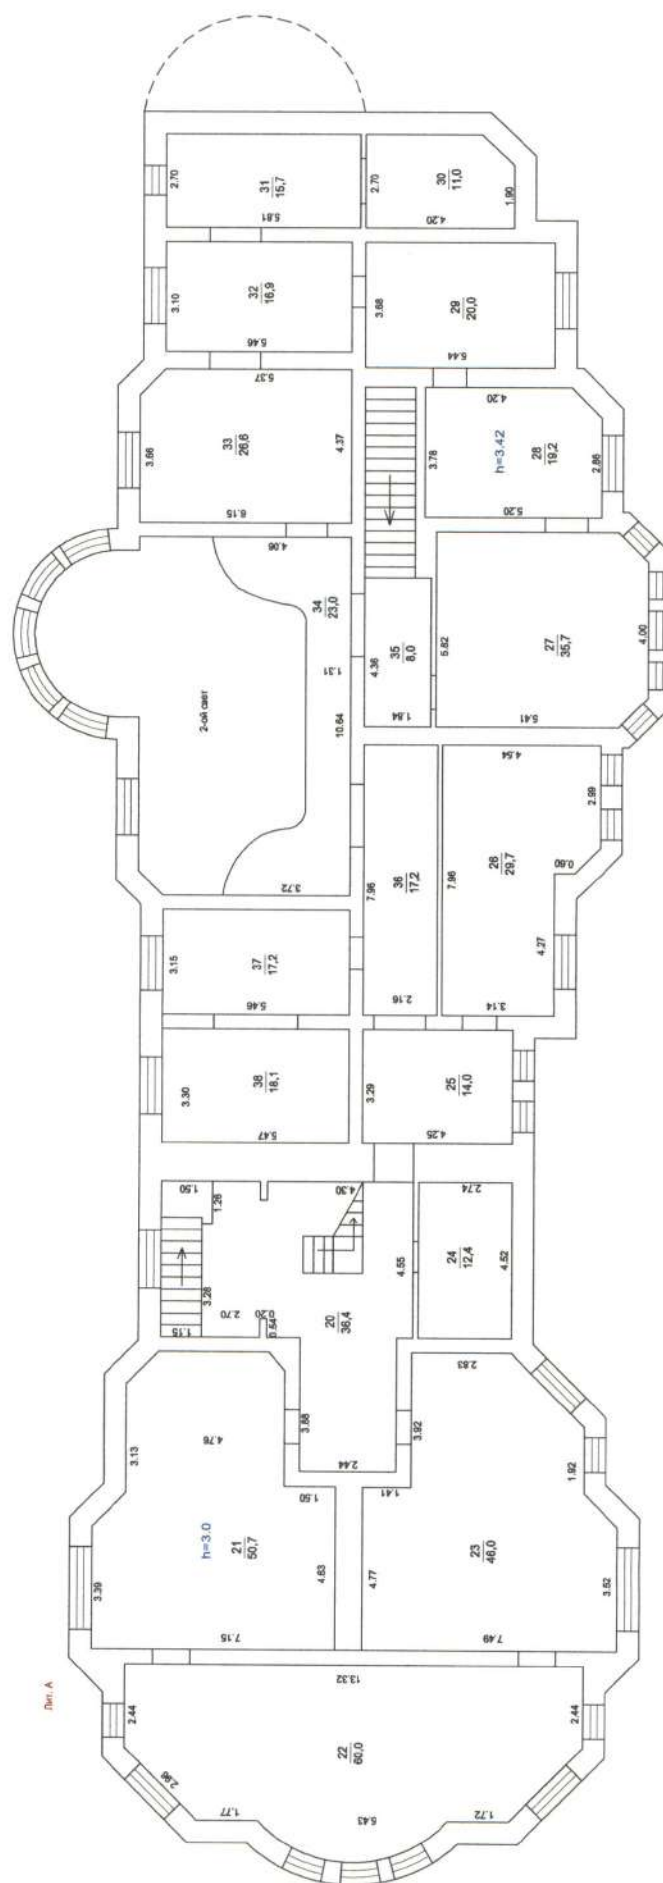


ПЛАД СОСТАВИЛ
" 16 " 04 2009 г.
Исполнял: Григорьев В.М.
Проверил: Пузанкова О.В.

maccurragh 1:150

ПОЭТАЖНЫЙ ПЛАН

строения инт. А2, в1

Находящегося в дер. Семеново, д. 17а

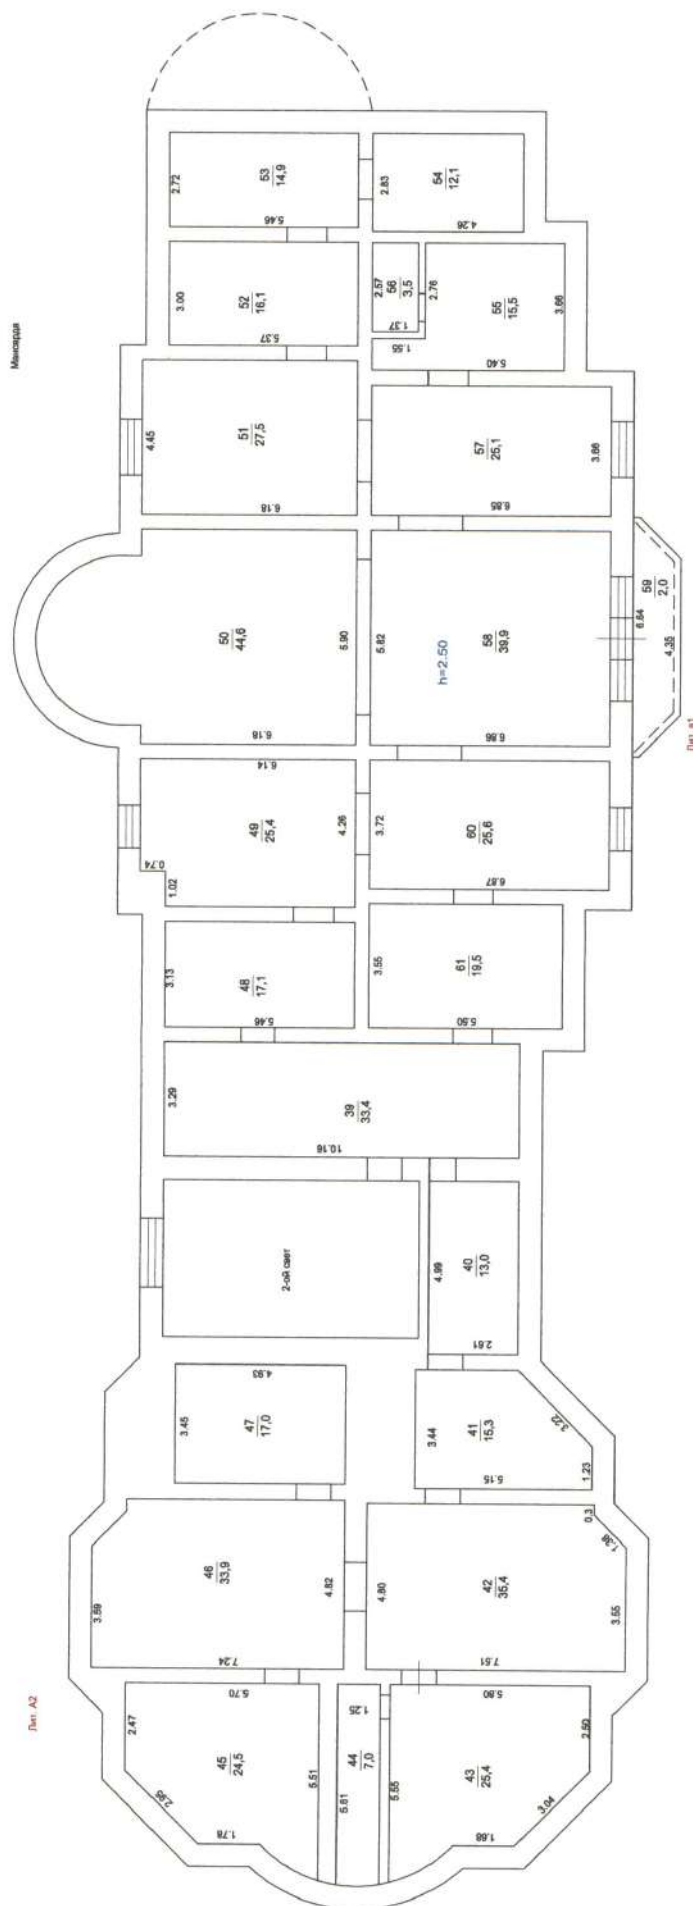

план составил

№ 16 " 04 2009 г.

Исполнил: Гриндаль В.М.

Проверил: Пузырева О.В.


масштаб 1:150

ПОЭТАЖНЫЙ ПЛАН

строения лит. А1

Находится в дер. Семеново, д. 17а

Порядок

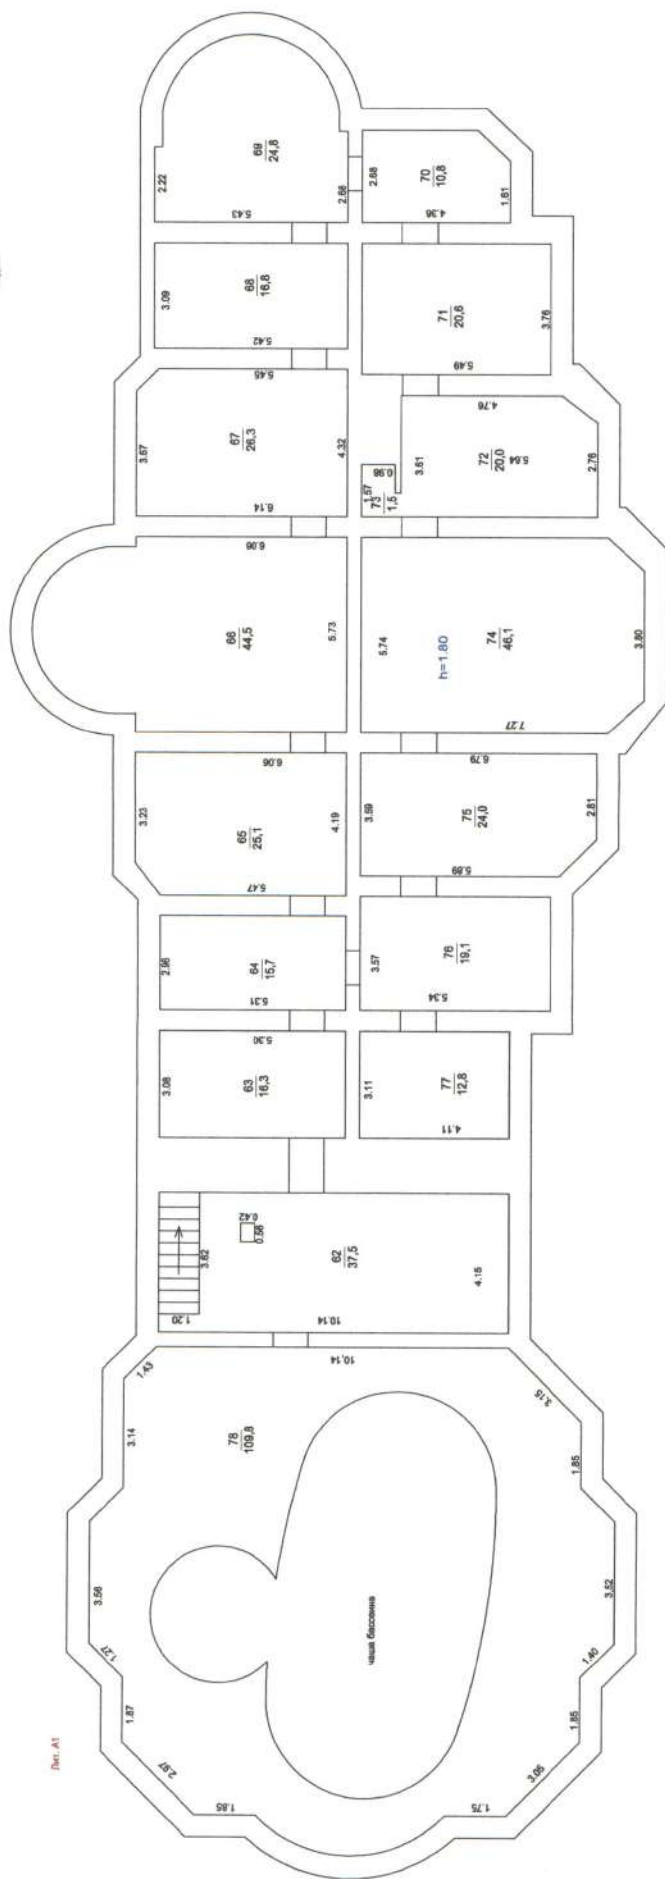

ПЛАН СОСТАВИЛ
"16" 04 2009 г.
Исполнил: Гриндиль В.М.
Проверил: Пузырева О.В.

масштаб 1:150

12

ПОЭТАЖНЫЙ ПЛАН
строения лит. Б
Находящегося в дер. Семенково, д. 17а

2 Этаж

Лит. Б



масштаб 1:100

план составил
" 16 " 04 2009 г.
Исполнил: Гриндуль В.М.
Проверил: Пузанкова О.В.

[Handwritten signatures]